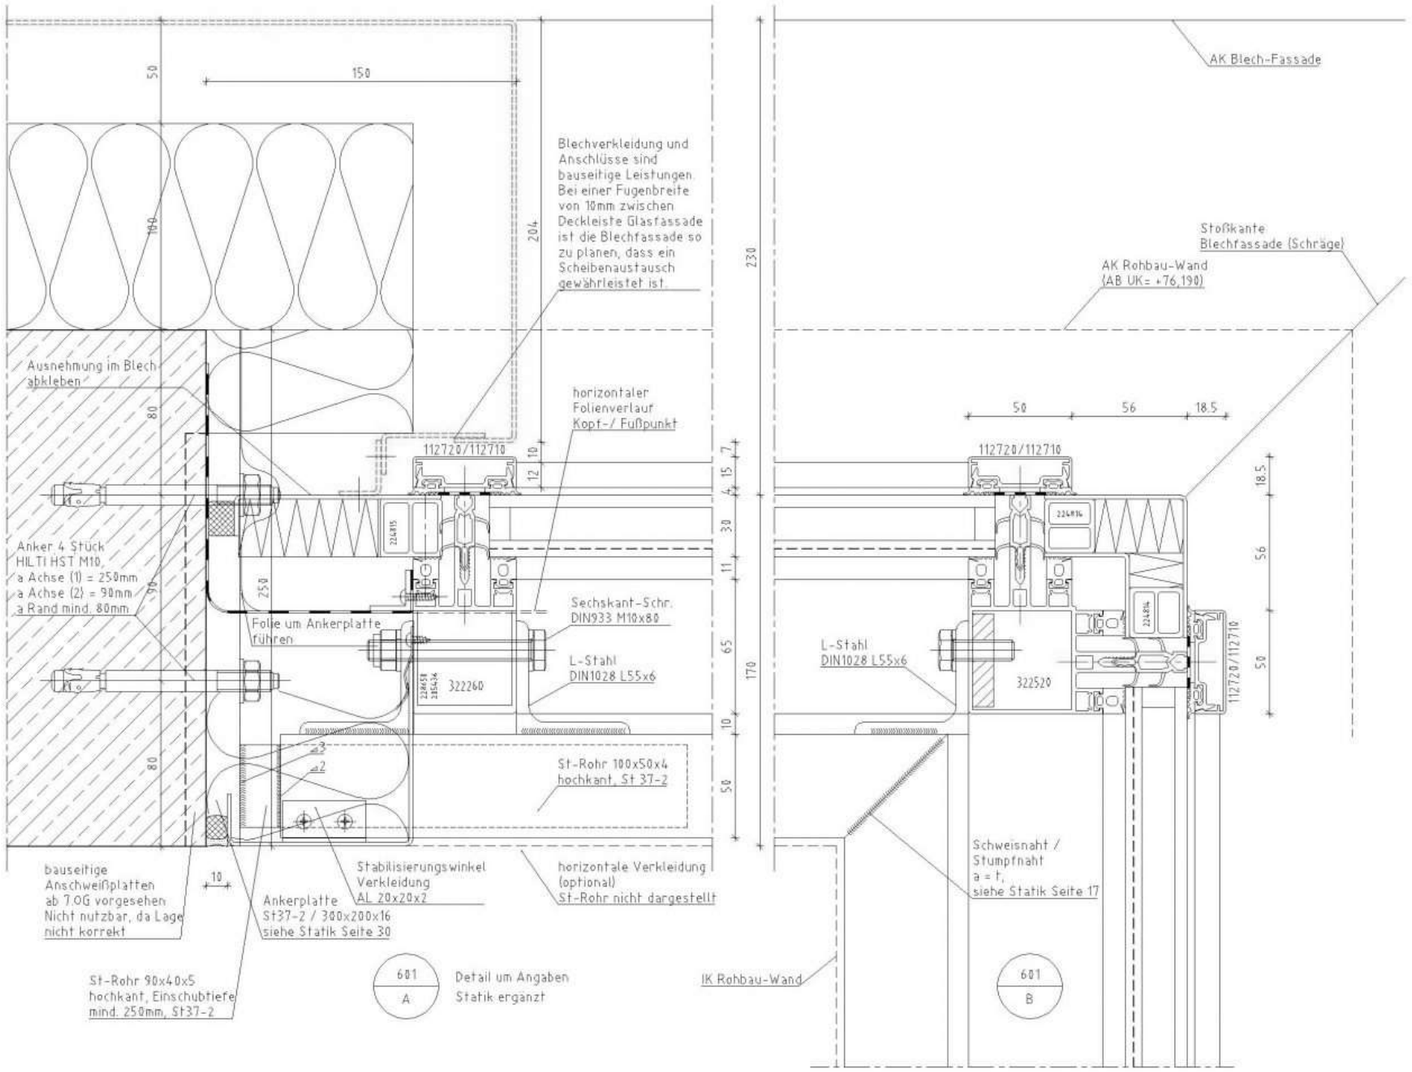

Detail Horizontalschnitt Aufzug-Fassade